방화터널 수배전반 단선결선도(변경후)

S= NONE

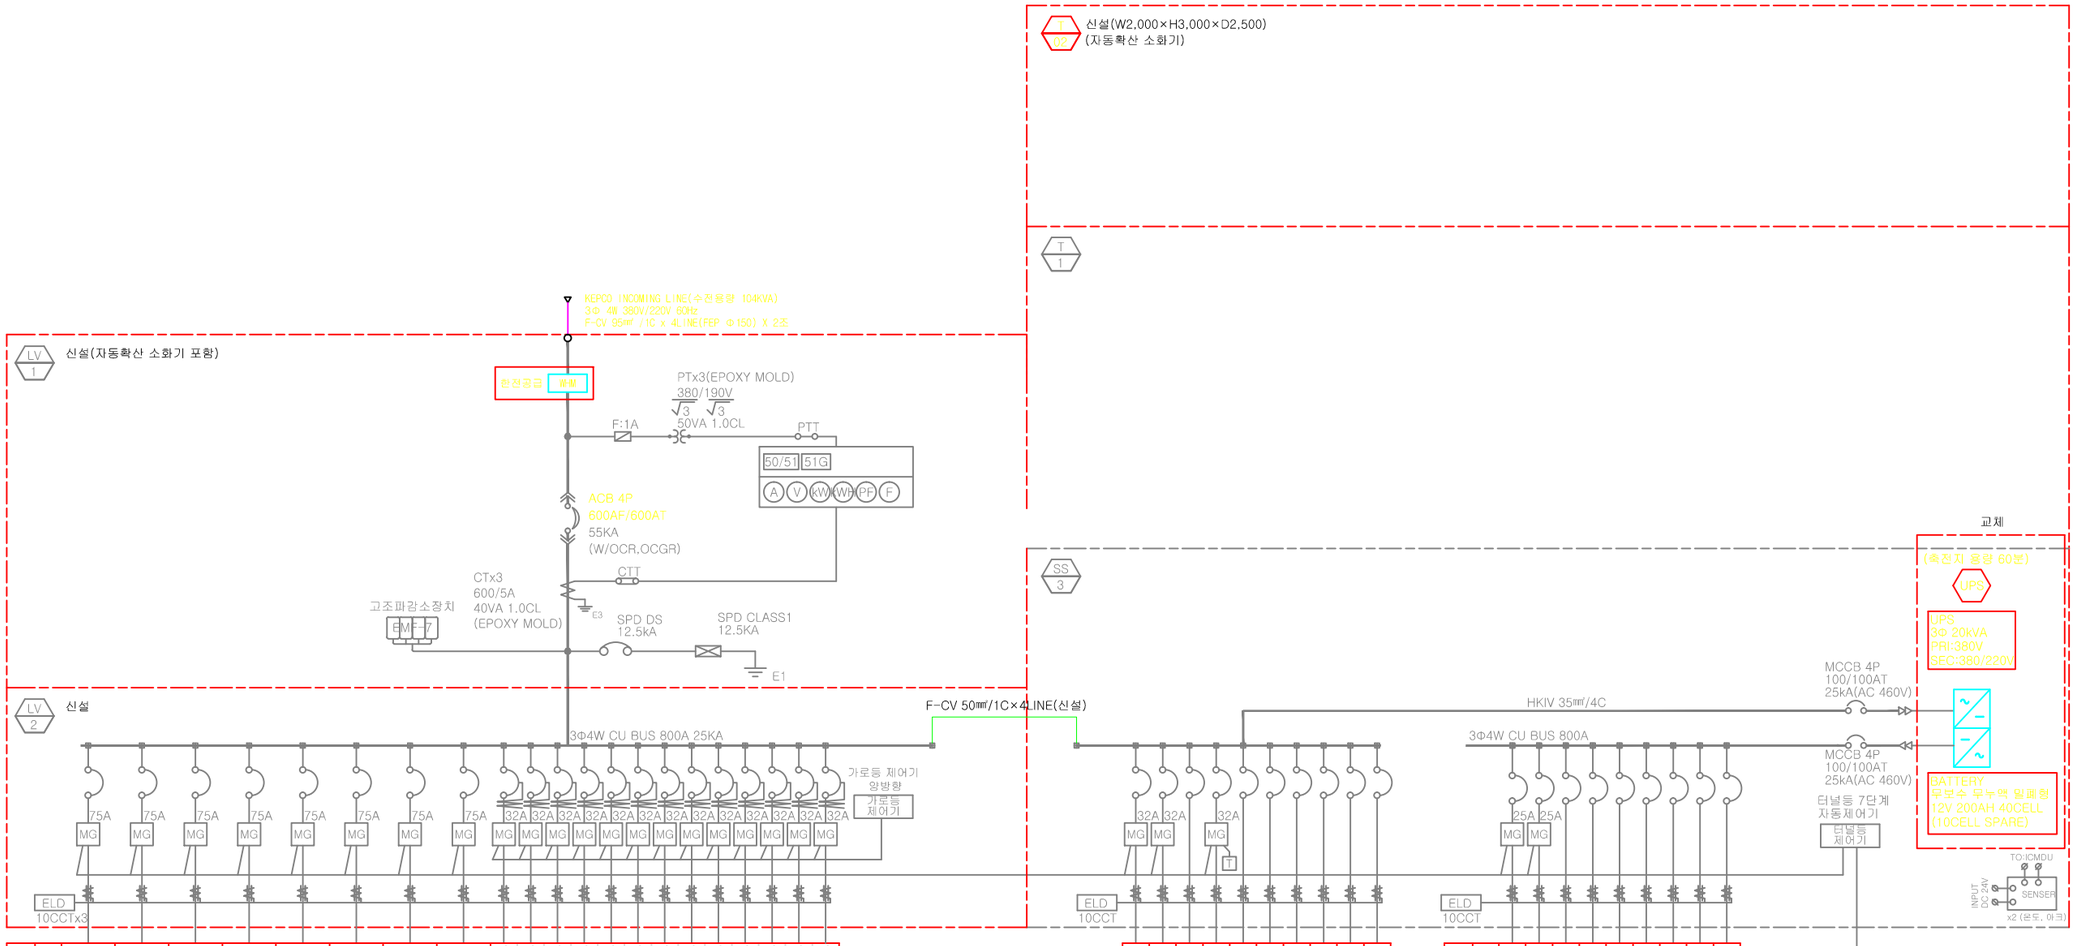

회로명	부하명	P	AF	AT	KA
C-U1	터널등화로 LED 75W×2 터널등화로 LED 150W×21	4	50	20	25
C-U2	터널등화로 LED 75W×2 터널등화로 LED 150W×21	4	50	20	25
CR-U1	터널등화로 LED 75W×3 터널등화로 LED 150W×21	4	50	20	25
CR-U2	터널등화로 LED 75W×2 터널등화로 LED 150W×21	4	50	20	25
C-D1	터널등화로 LED 75W×2 터널등화로 LED 150W×21	4	50	20	25
C-D2	터널등화로 LED 75W×2 터널등화로 LED 150W×21	4	50	20	25
CR-D1	터널등화로 LED 75W×3 터널등화로 LED 150W×21	4	50	20	25
CR-D2	터널등화로 LED 75W×2 터널등화로 LED 150W×22	4	50	20	25
L1A	옥외가로등 MH 200W×5	2	30	30	50 ELB
L1B	옥외가로등 MH 200W×5	2	30	30	50 ELB
L2A	옥외가로등 MH 200W×3	2	30	30	50 ELB
L2B	옥외가로등 MH 200W×3	2	30	30	50 ELB
L3A	옥외가로등 MH 200W×3	2	30	30	50 ELB
L3B	옥외가로등 MH 200W×3	2	30	30	50 ELB
L4A	옥외가로등 MH 200W×3	2	30	30	50 ELB
L4B	옥외가로등 MH 200W×2	2	30	30	50 ELB
L7A	옥외가로등 MH 150W×11	2	30	30	50 ELB
L7B	옥외가로등 MH 150W×10	2	30	30	50 ELB
L8A	옥외가로등 MH 150W×12	2	30	30	50 ELB
L8B	옥외가로등 MH 150W×11	2	30	30	50 ELB
SP	SPARE				50 ELB

회로명	부하명	P	AF	AT	KA
N-U2	터널등화로 LED 75W×44	4	100	20	25
N-D1	터널등화로 LED 75W×48	4	100	20	25
LV-UPS	UPS	4	100	100	25
RMP-A1,C,D	교량정경등 FUL 20W	4	100	30	25
SP	SPARE	4	100	30	25
SP	SPARE	4	100	30	25
SP	SPARE	4	100	20	25
SP	SPARE	4	100	20	25
SP	SPARE	4	100	20	25
SP	SPARE	4	100	20	25

회로명	부하명	P	AF	AT	KA
NE-U1	터널등화로 LED 75W×44(상시 점등)	4	100	20	25
NE-D2	터널등화로 LED 75W×48(상시 점등)	4	100	20	25
SP	SPARE	4	100	20	25
SP	SPARE	4	100	20	25
FU,FD	소화기 표시등	2	100	20	50
SU,SD	시선유도등	2	100	20	50
EU	유도표시등(상행)	2	100	20	50
ED	유도표시등(하행)	2	100	20	50
통신	자하재방송,CCTV 장비	2	100	20	50

발주처	공사명	용역사	설계참여자			도면명	축척	도면번호
			사업책임자	분야별책임자	설계자			
시설공단 로고.png ??????	방화터널 조명설비 교체공사	주식회사 청석전기이엔지 CHUNGSUK ELEC. ENGINEERING	박 종 수	원 남 규	강 상 우	방화터널 수배전반 단선결선도(변경후)	NONE	E-004